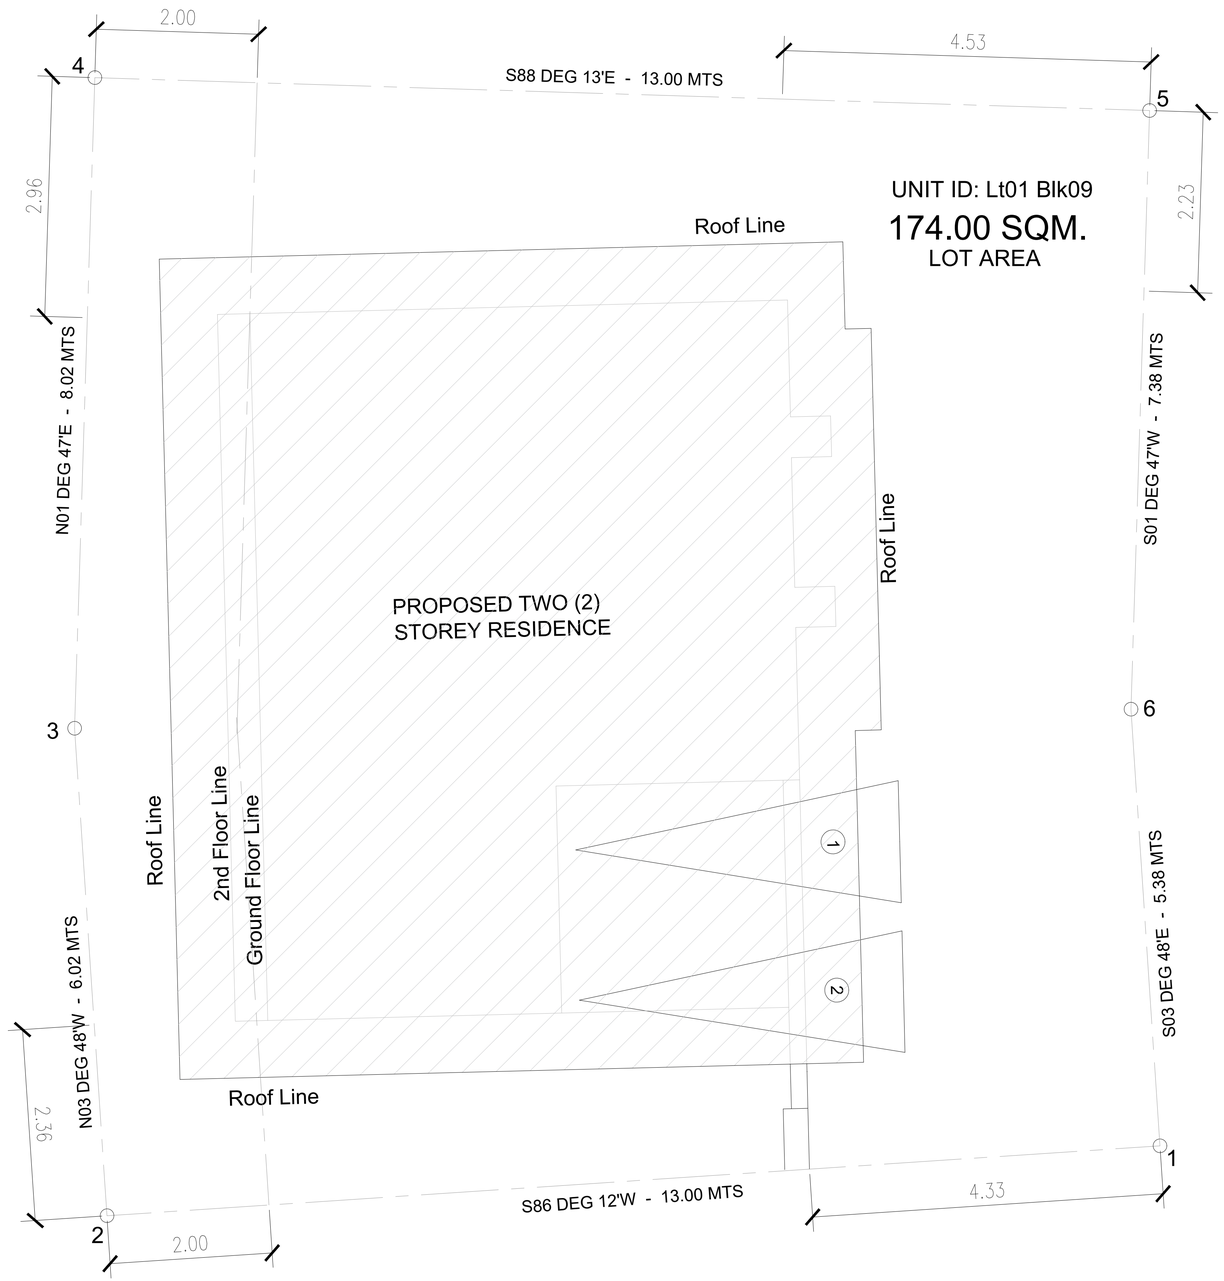

LOT PLAN

SCALE: 1:100 MTS

REPUBLIC OF THE PHILIPPINES
DEPARTMENT OF PUBLIC WORKS AND HIGHWAYS
OFFICE OF THE BUILDING OFFICIAL

BACOOR, CAVITE
DISTRICT / CITY / MUNICIPALITY

TECHNICAL DESCRIPTION:

BEARING	DISTANCE
S86 DEG 12'W	13.00 MTS
N03 DEG 48'W	6.02 MTS
N01 DEG 47'E	8.02 MTS
S88 DEG 13'E	13.00 MTS
S01 DEG 47'W	7.38 MTS
S.3 DEG 48'E	5.38 MTS

PROJECT TITLE:

LOCATION:

BELLEFORT VILLAGE
Molino, Bacoor Cavite

OWNER:

ADDRESS:

SHEET CONTENT:

LOT PLAN

DESIGNED BY:	APPROVED BY: MRO
DRAWN BY: FOB	DATE: 012626
CHECKED BY:	

CONTRACTOR:

breighton