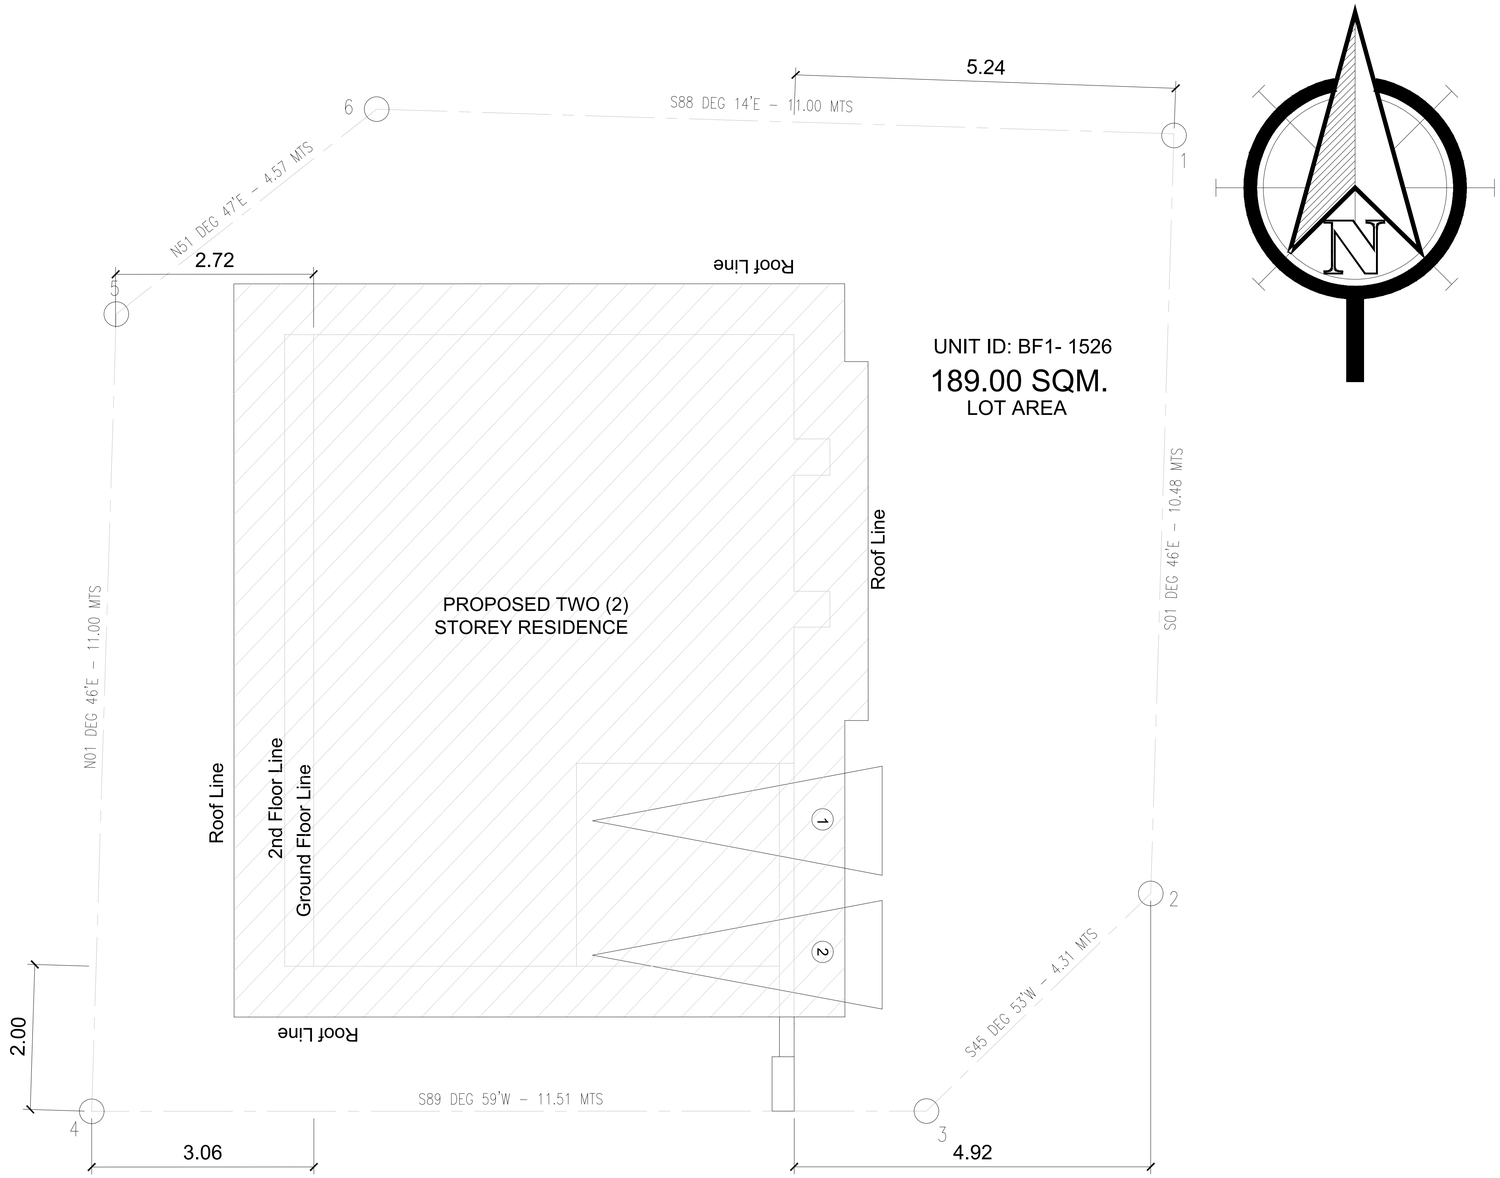

LOT PLAN

SCALE: MTS.

REPUBLIC OF THE PHILIPPINES
DEPARTMENT OF PUBLIC WORKS AND HIGHWAYS
OFFICE OF THE BUILDING OFFICIAL

BACOOR, CAVITE
DISTRICT / CITY / MUNICIPALITY

TECHNICAL DESCRIPTION:

BEARING	DISTANCE
S01 DEG 46'E	10.48 MTS
S45 DEG 53'W	4.31 MTS
S89 DEG 59'W	11.51 MTS
N01 DEG 46'E	11.00 MTS
N51 DEG 47'E	4.57 MTS
S88 DEG 14'E	11.00 MTS

PROJECT TITLE:

VIVIENNE HOUSE MODEL

LOCATION:

BELLEFORT ESTATE
Molino, Bacoor Cavite

OWNER:

ADDRESS:

SHEET CONTENT:

LOT PLAN

DESIGNED BY:		APPROVED BY:	MRO
DRAWN BY:	FOB	DATE:	060225
CHECKED BY:			

CONTRACTOR:

breighton